
面料仓货架布置草稿 v0（二~七层标准层） 单格≈2.0×1.95m ×2层 仓位 406 格（西区 194 / 东区 212） 货架占地率 40%

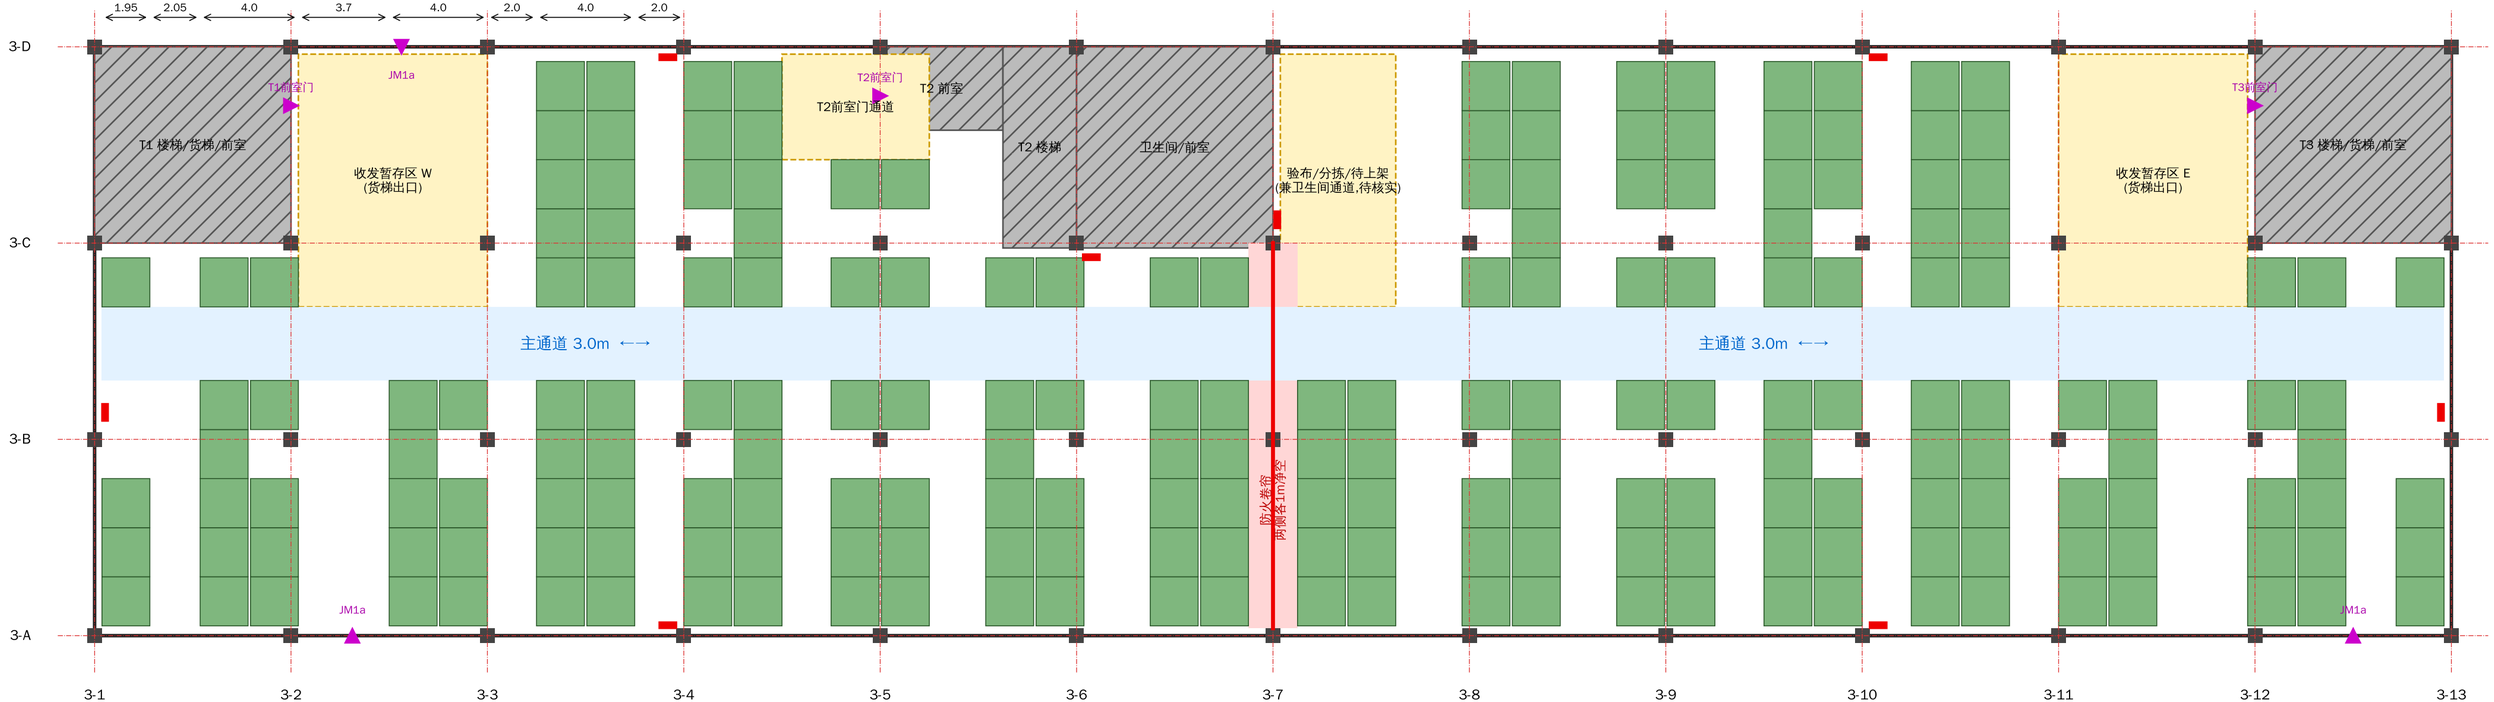

图例：绿=货架单格(每格2层) 灰斜线=核心筒 黄虚线=功能区 红块=消火栓(估) 紫箭头=门 浅蓝=主通道 粉=防火卷帘净空带 尺寸单位 m（标注）/mm（坐标） ——草稿，柱/门/消火栓需现场复核